

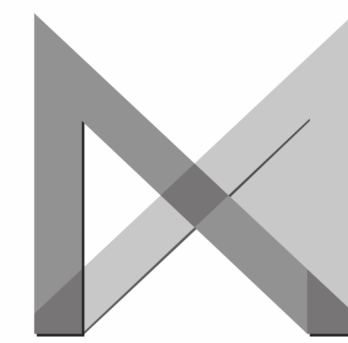
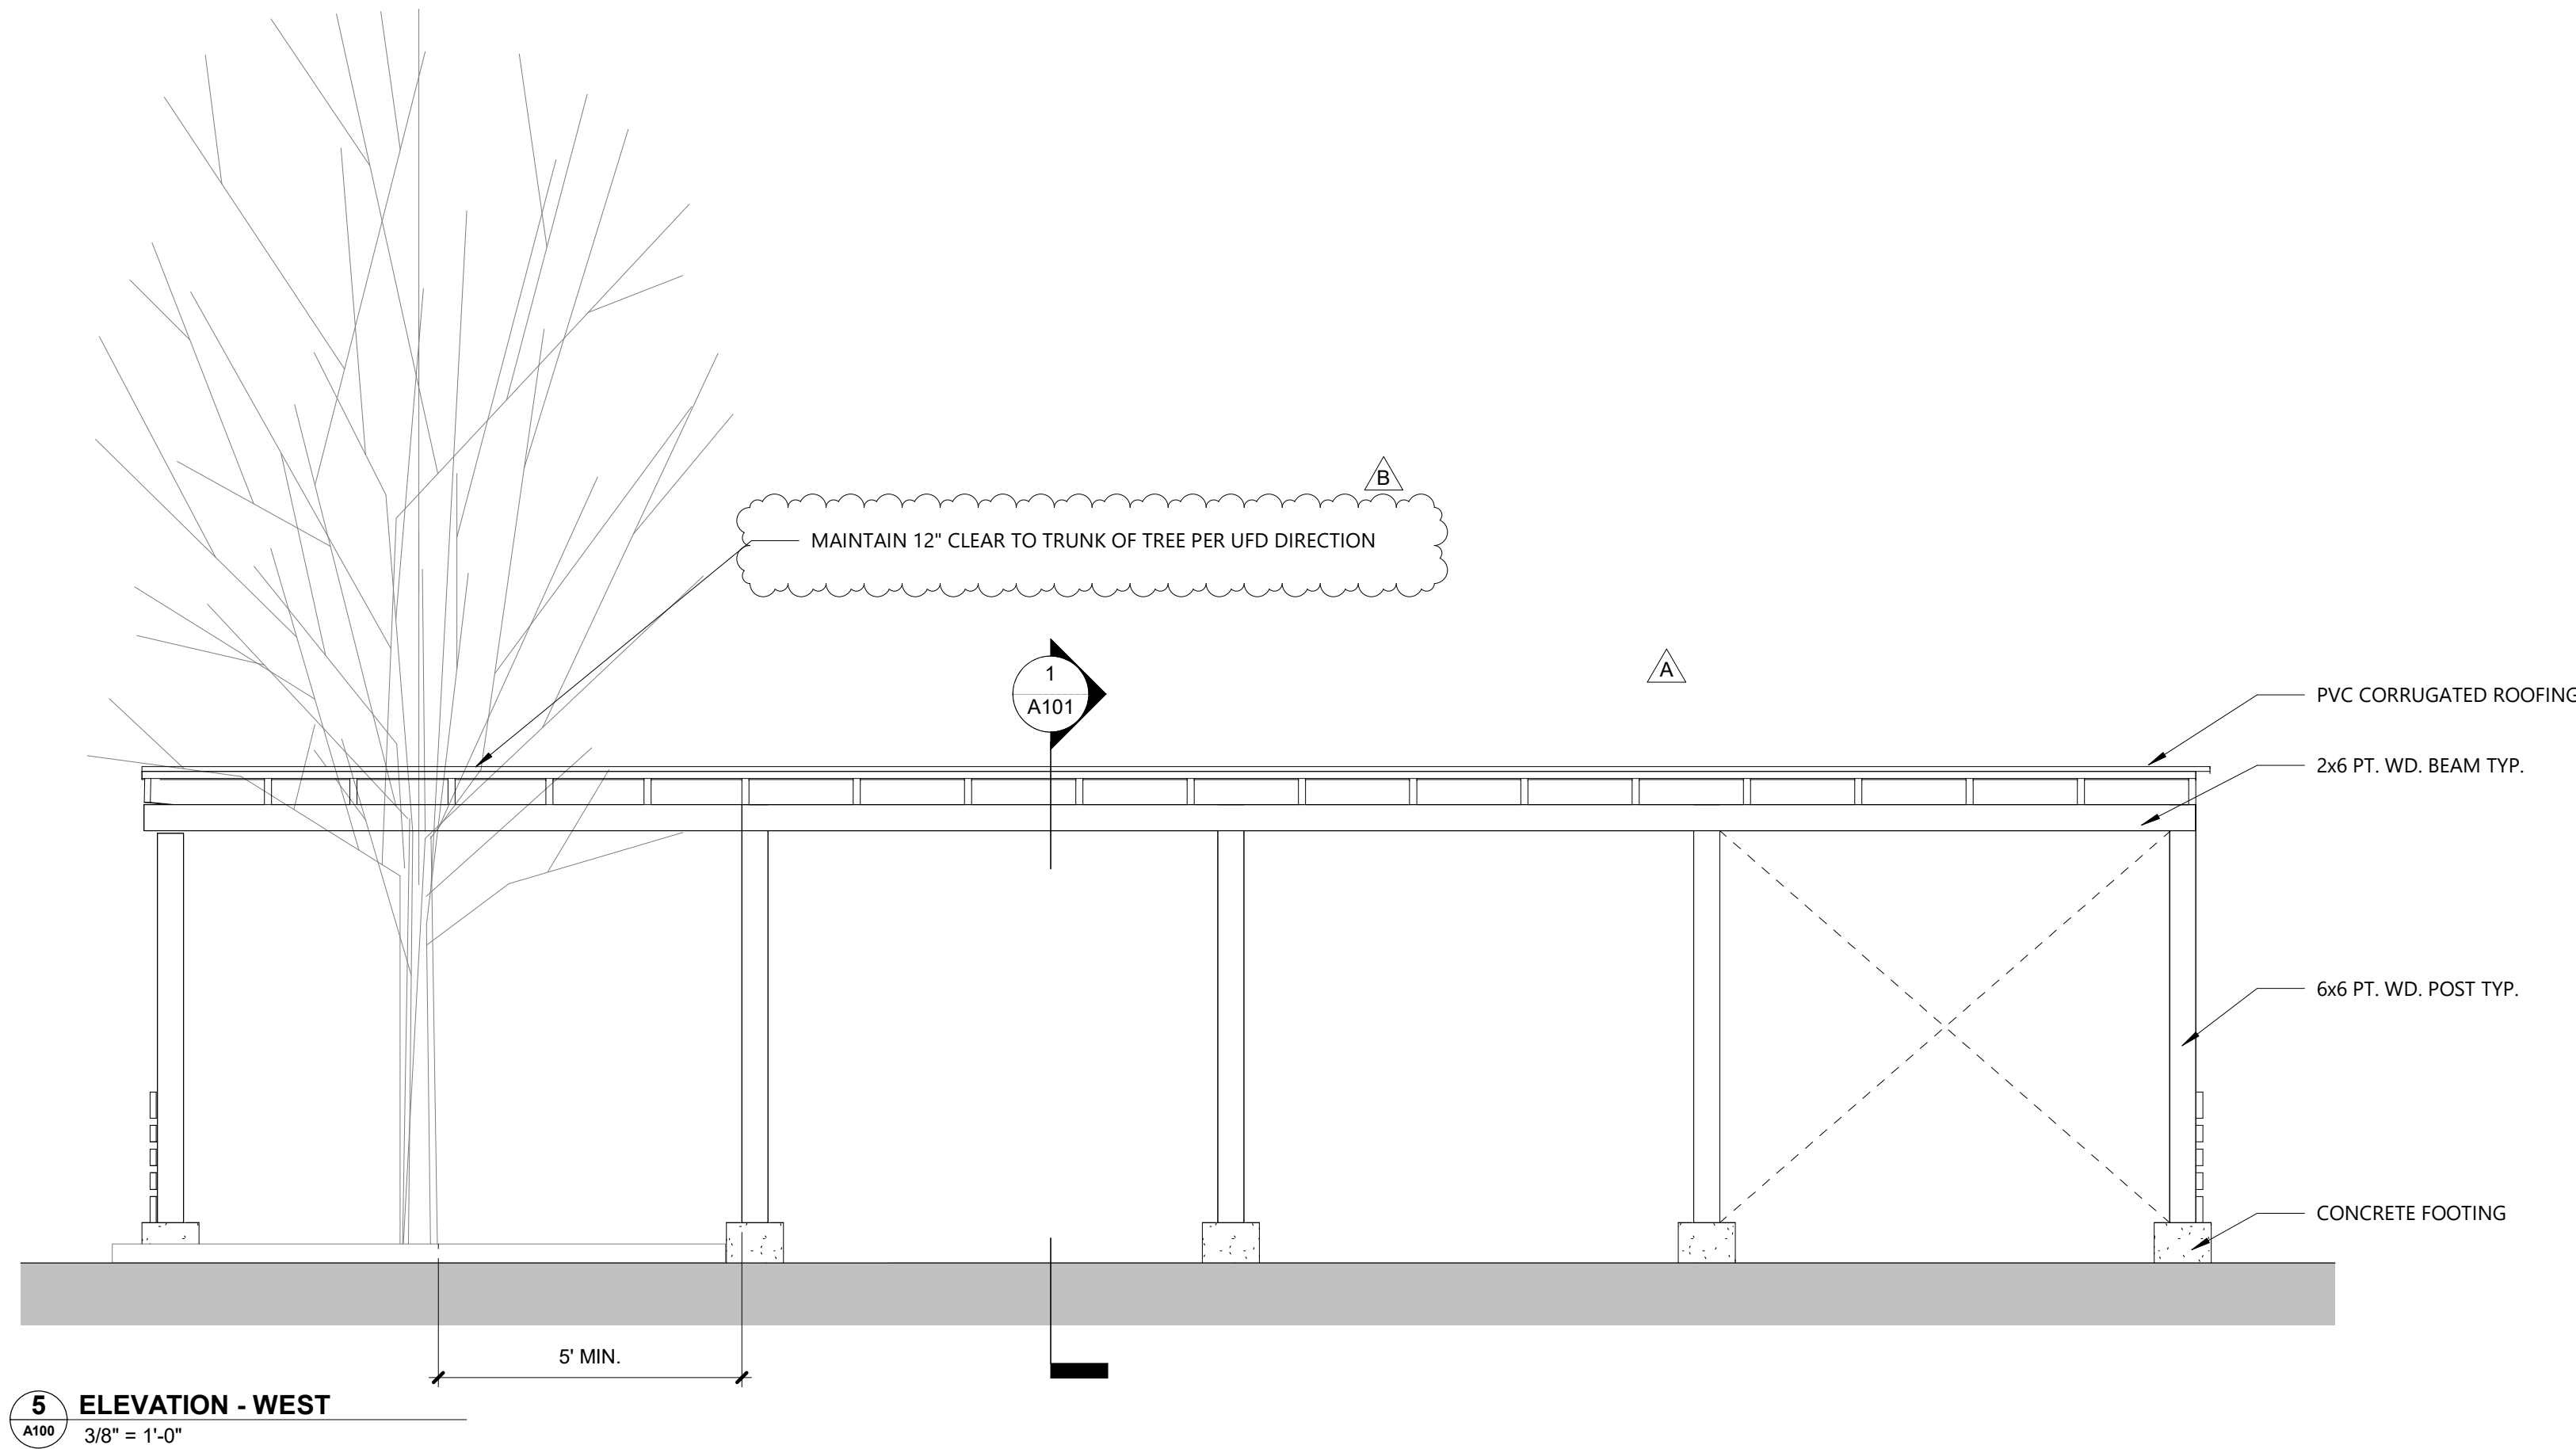
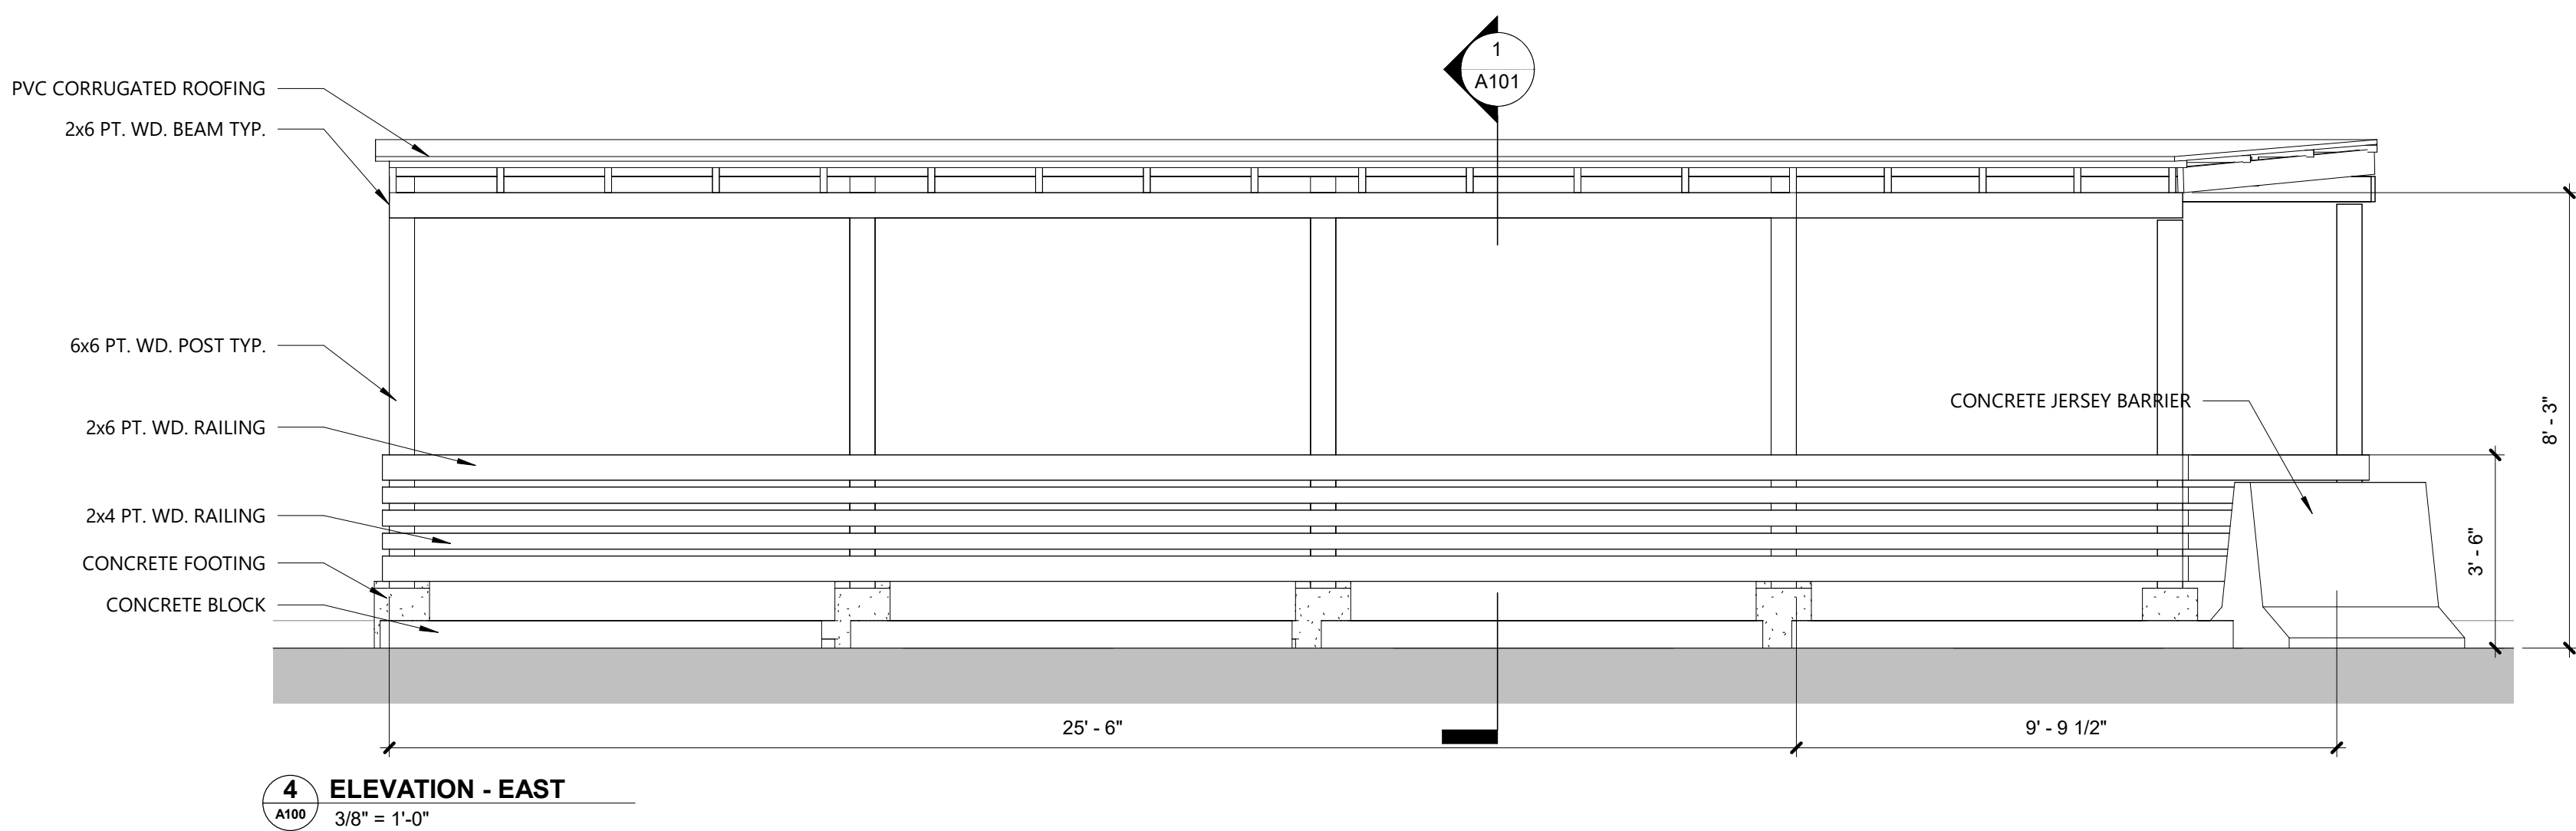
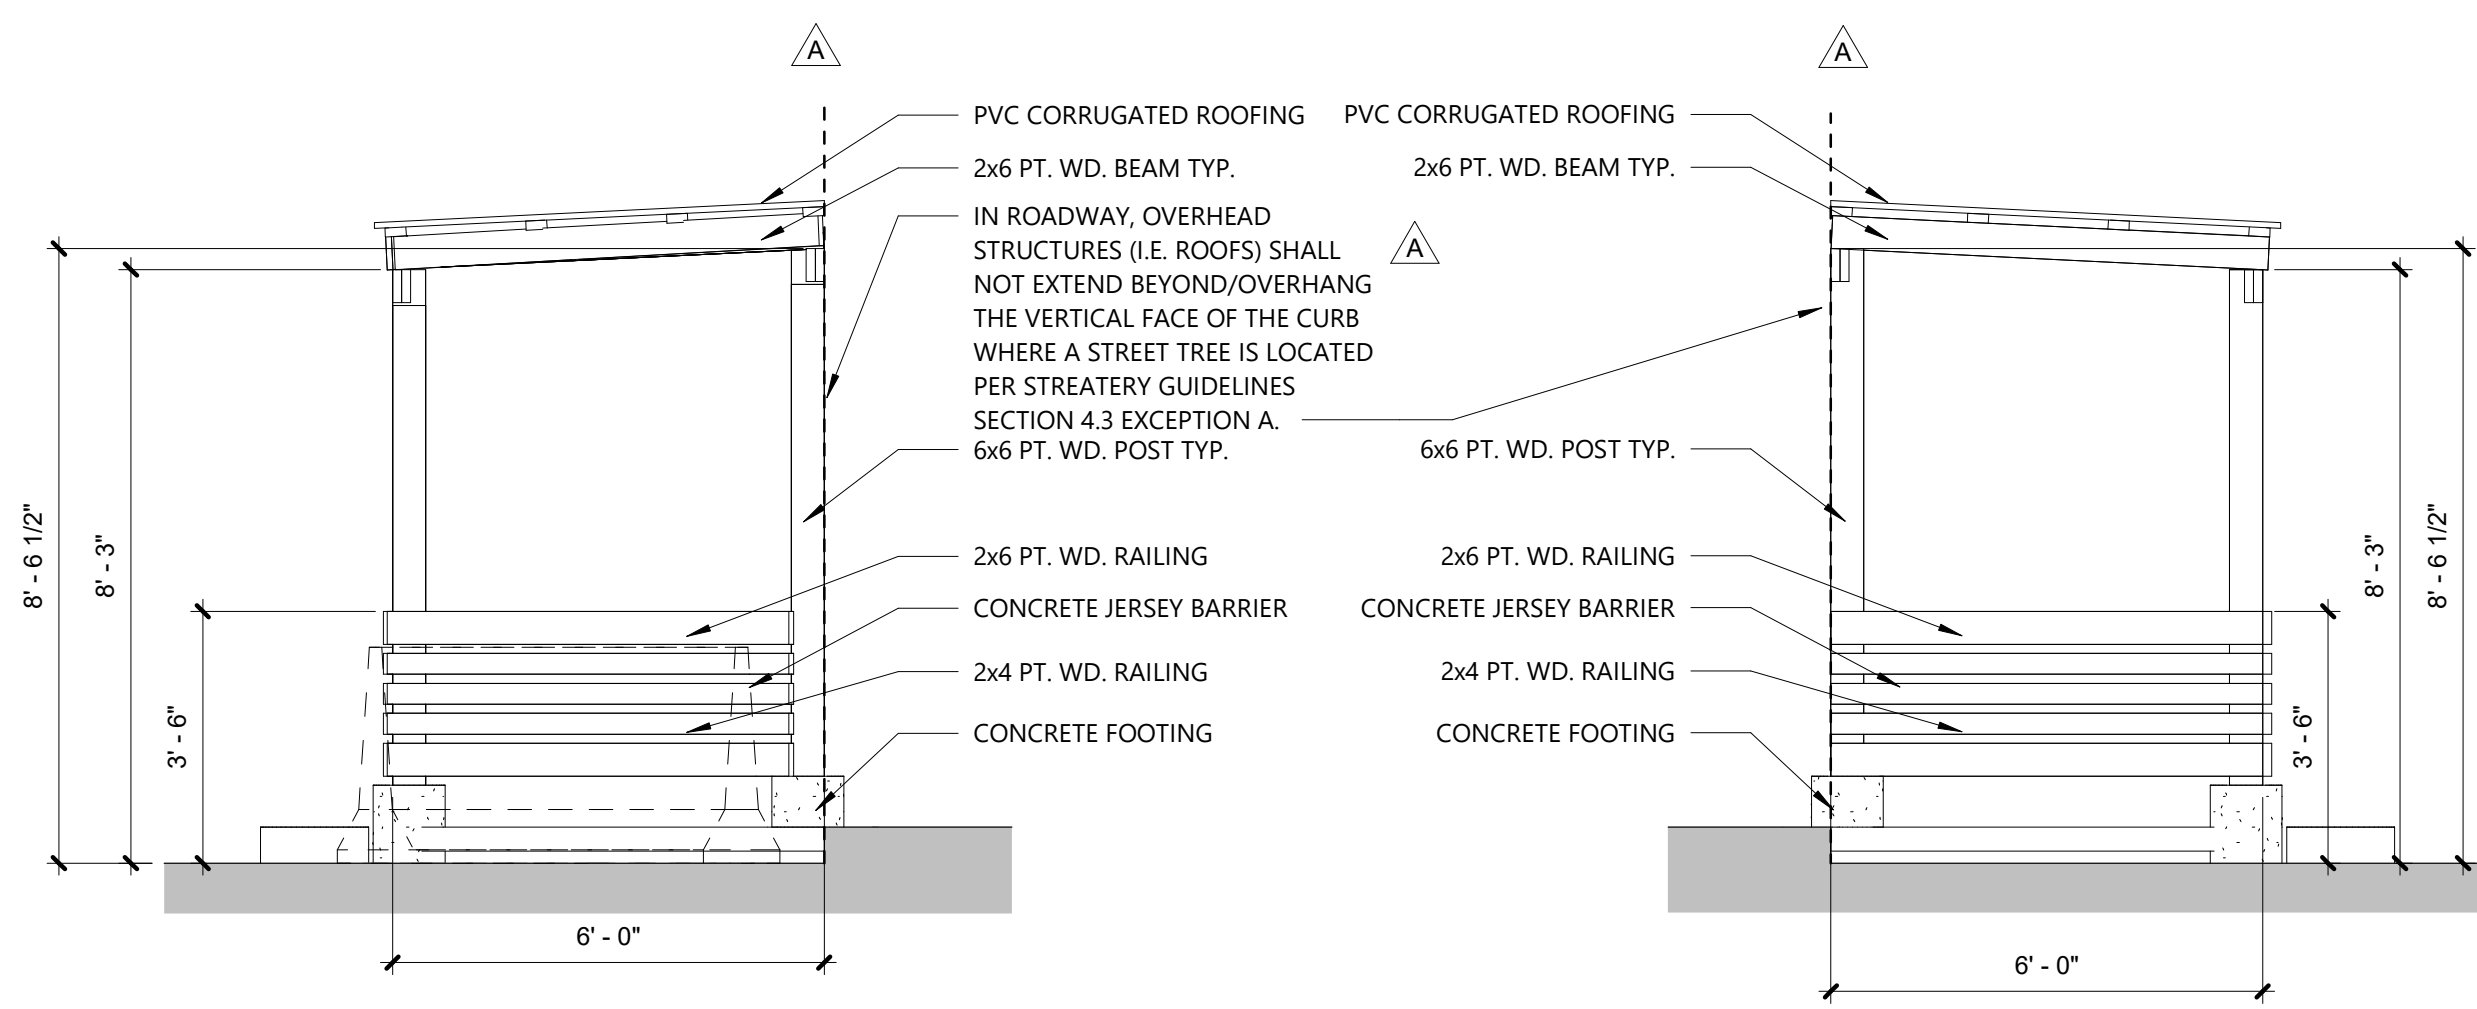


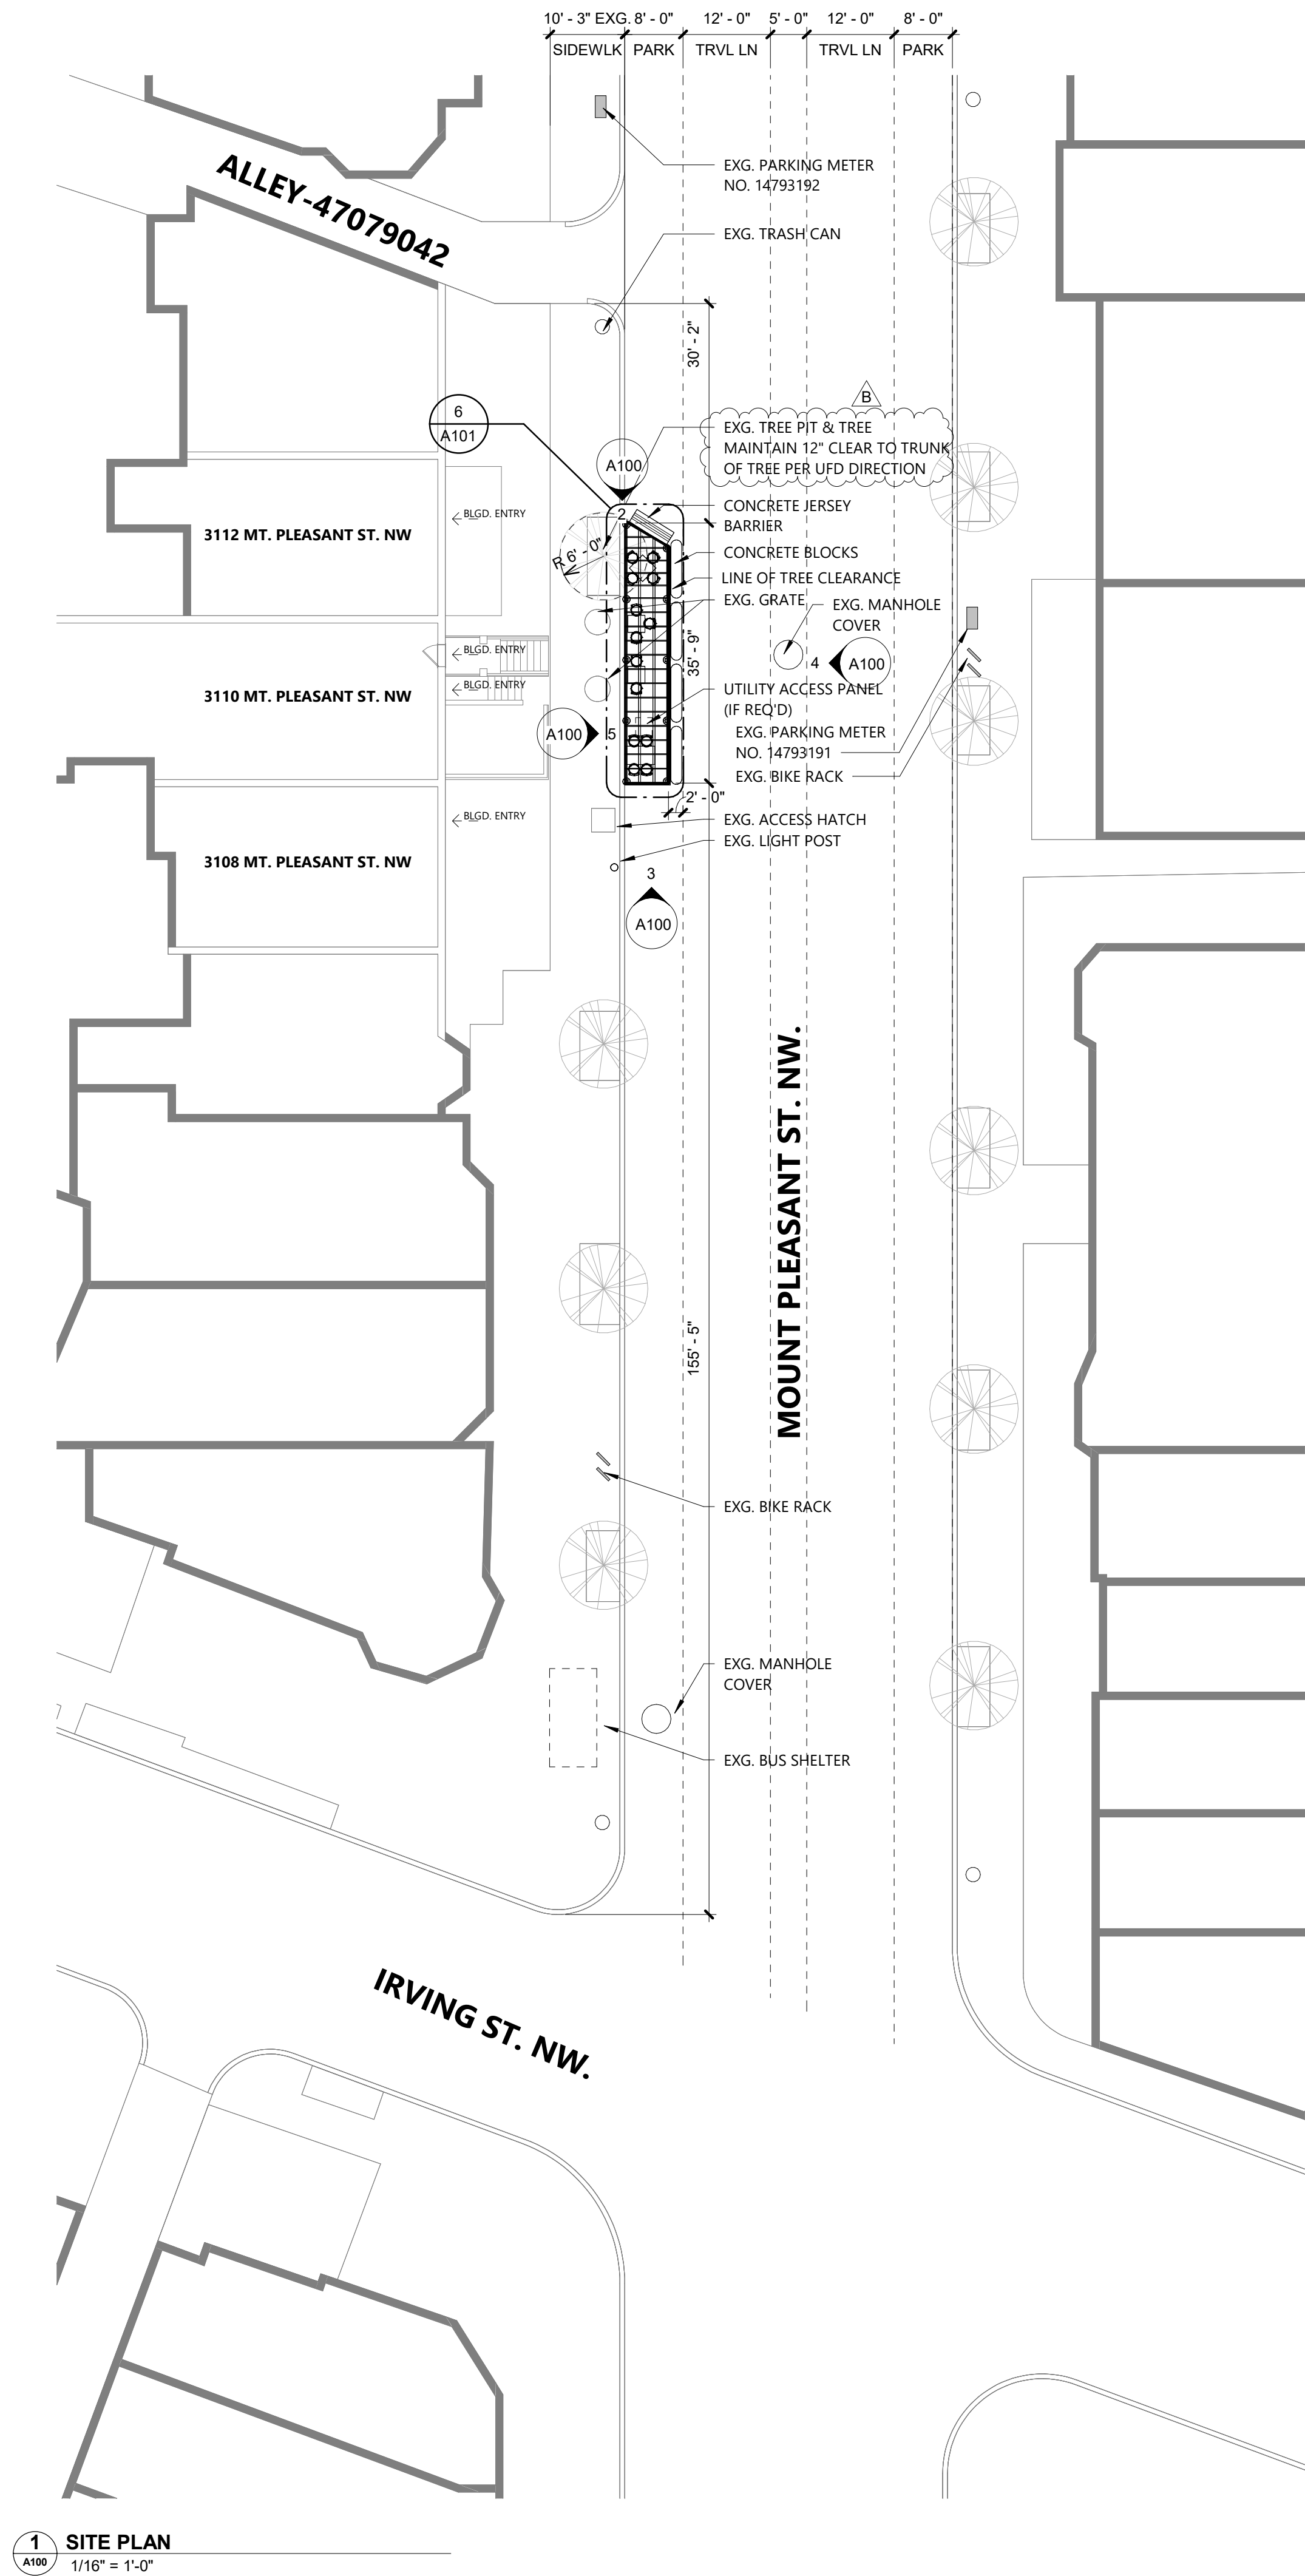

ANDREW METZLER, AIA
10701 JAMAICA DRIVE
SILVER SPRING, MD 20902

PROFESSIONAL SEAL

PROFESSIONAL CERTIFICATION:
I HEREBY CERTIFY THAT THESE DOCUMENTS
WERE PREPARED OR APPROVED BY ME, AND
THAT I AM A DULY LICENSED PROFESSIONAL
ARCHITECT UNDER THE LAWS OF
WASHINGTON D.C.

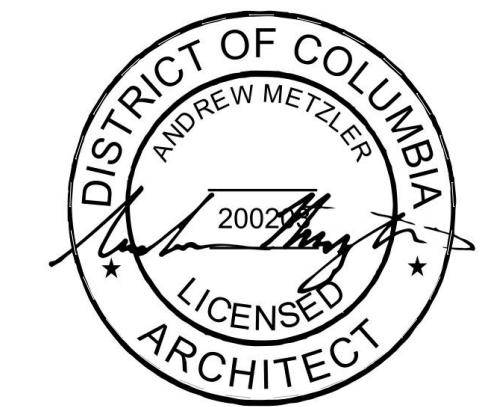

LICENSE NO:ARC100920 EXP:04.30.2026

ISSUANCES

#	DESCRIPTION	DATE
	ISSUE FOR STREARTY DESIGN PERMIT	11.10.25
A	REVISION A	01.11.26
B	REVISION B	02.28.26

REVISIONS

#	DESCRIPTION	DATE

MARTHA DEAR
STREARTY

3110 MT PLEASANT ST NW
WASHINGTON, D.C. 20010

SITE PLAN &
ELEVATIONS

A100

PROJECT NUMBER 25-023

DATE 11.10.25

SCALE As indicated

ANDREW METZLER, AIA 2025 ©